

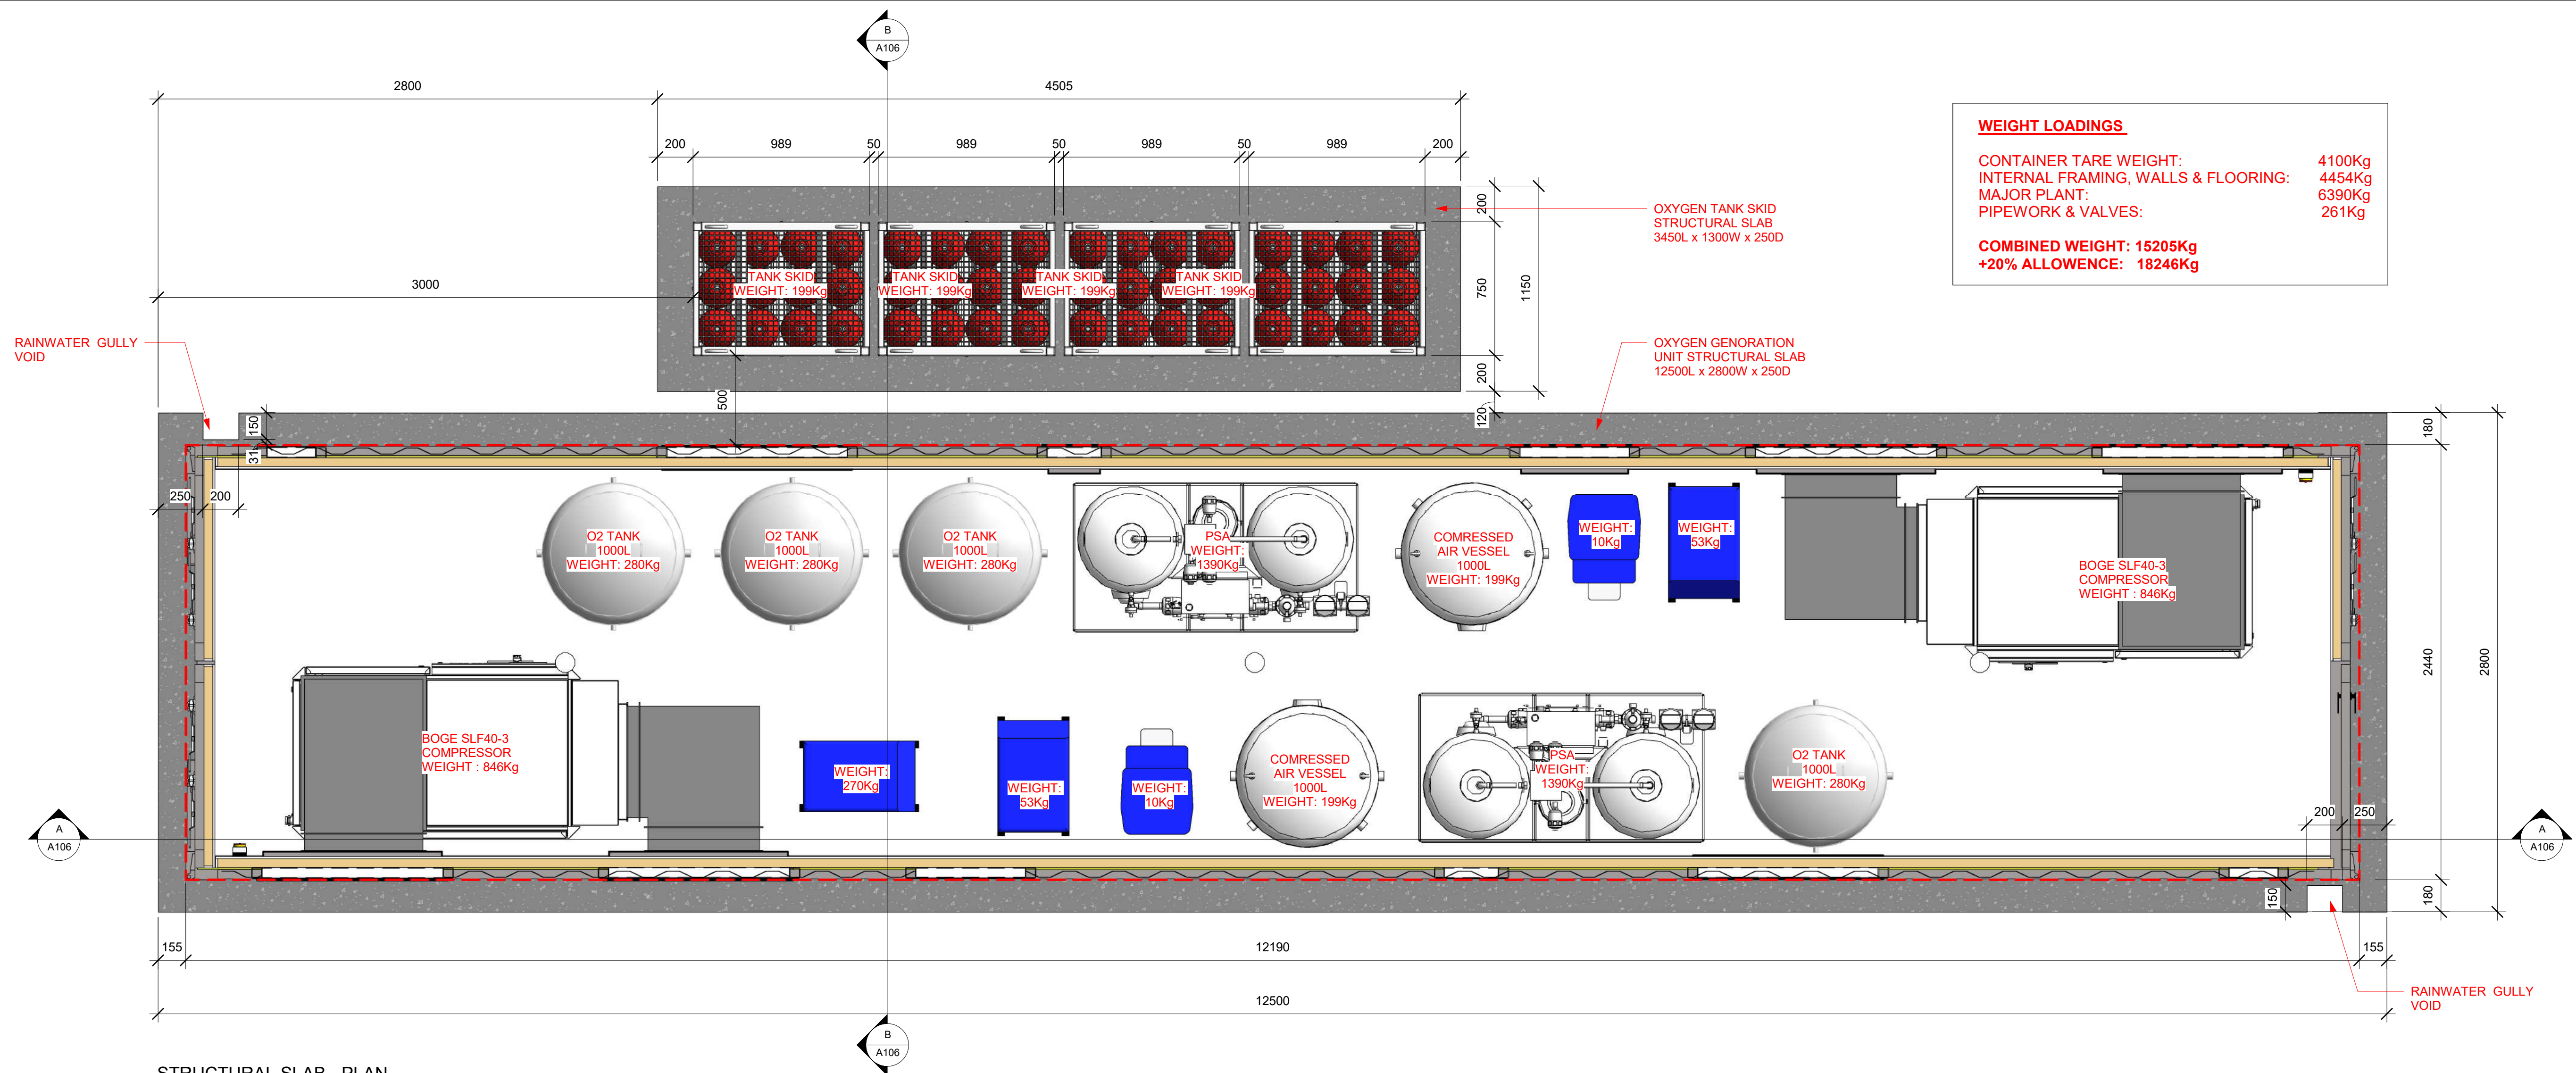


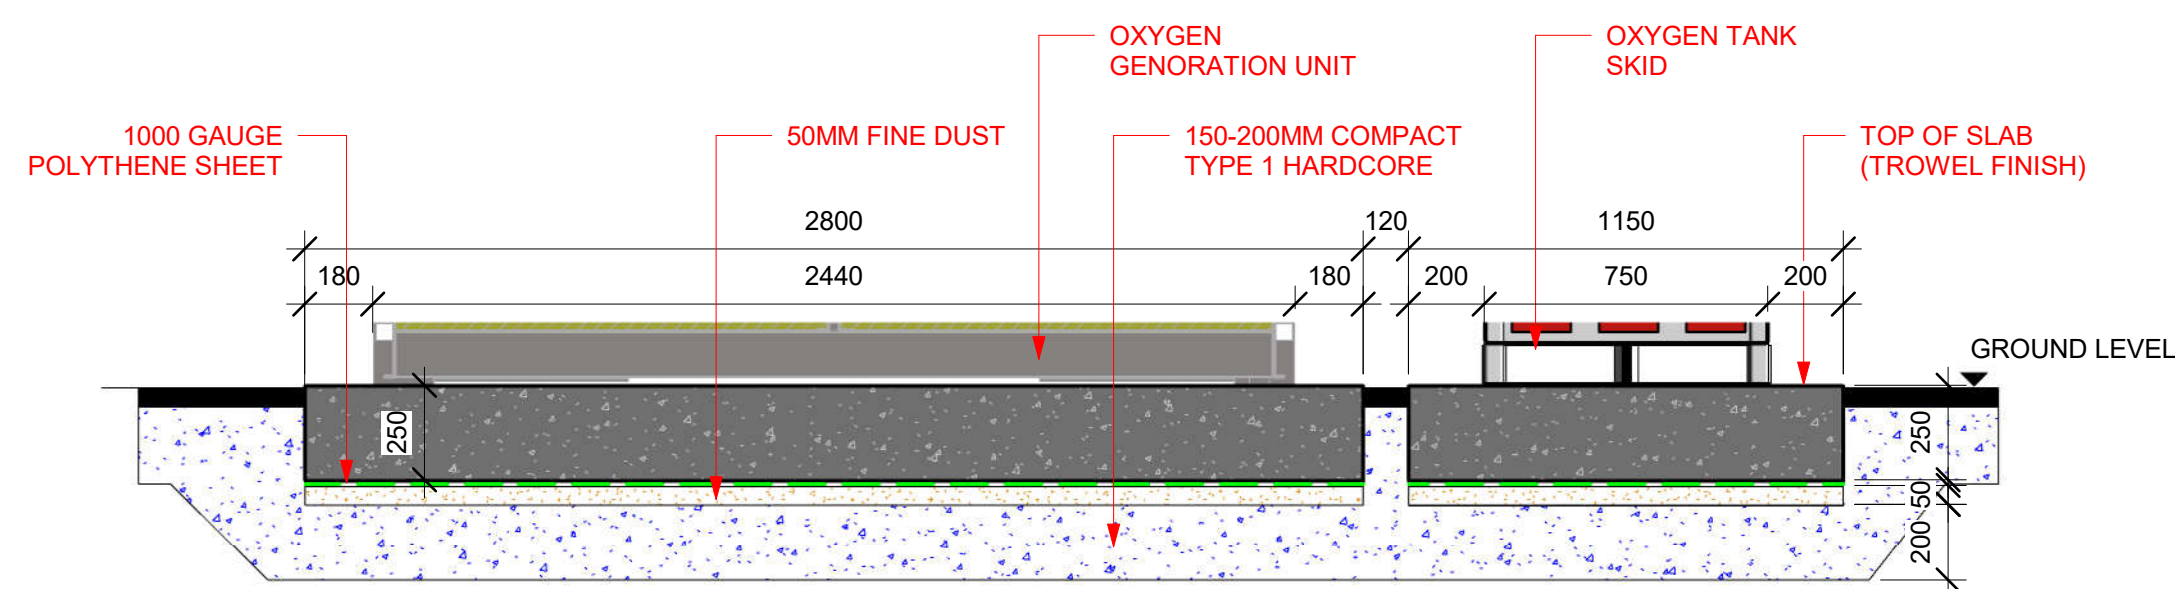

WEIGHT LOADINGS	
CONTAINER TARE WEIGHT:	4100Kg
INTERNAL FRAMING, WALLS & FLOORING:	4454Kg
MAJOR PLANT:	6390Kg
PIPEWORK & VALVES:	261Kg
COMBINED WEIGHT: 15205Kg	
+20% ALLOWENCE: 18246Kg	

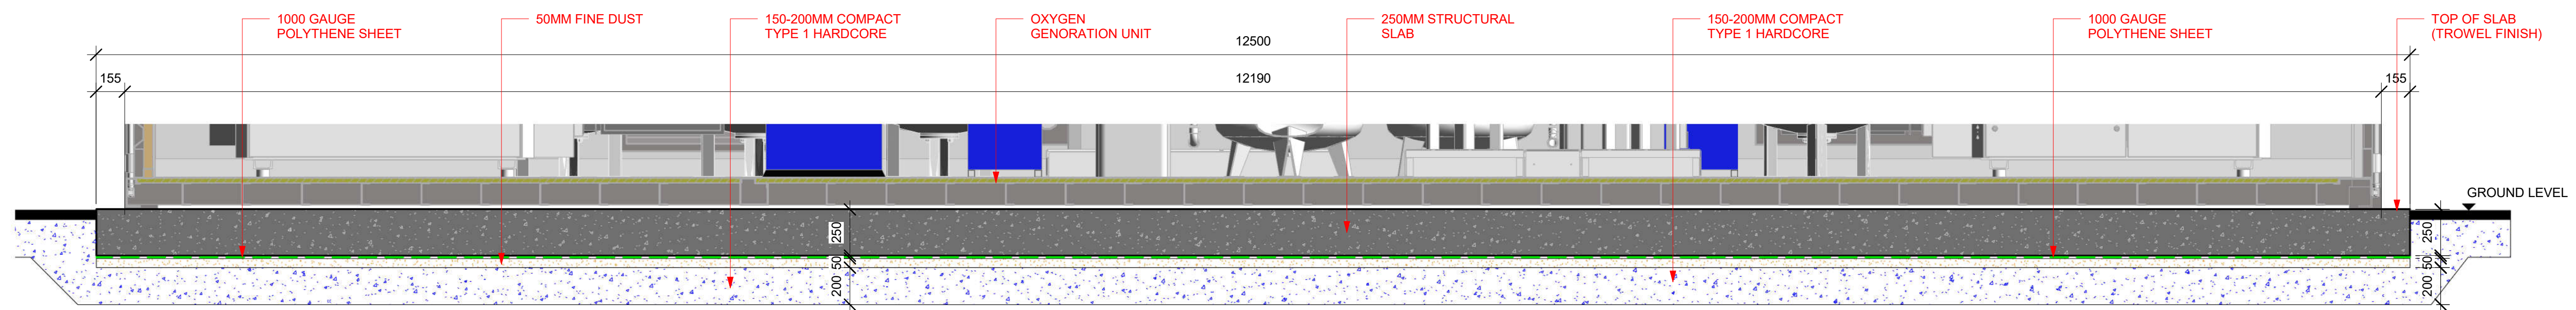

STRUCTURAL SLAB - 3D PERSPECTIVE

THIS DRAWING IS COPYRIGHT OF ALTERNATIVE HEAT LTD.
THIS DRAWING MAY NOT BE COPIES OR REPRODUCED WITHOUT THE CONSENT OF ALTERNATIVE HEAT LTD.
THIS DRAWING IS FOR USE ON THIS PROJECT ONLY UNLESS CONTRACTUALLY OTHERWISE STATED.
DO NOT SCALE THIS DRAWING (PRINTED OR ELECTRONIC VERSIONS).
THIS DRAWING IS FOR SPATIAL CO-ORDINATION PURPOSES ONLY. ALL CONTRACTORS ARE RESPONSIBLE FOR SETTING OUT AND MUST CHECK ALL LEVELS AND DIMENSIONS PRIOR TO INSTALLATION / CONSTRUCTION.
ALL OTHER DESIGN ELEMENTS, WHERE INDICATED, HAVE BEEN IMPORTED FOR EXTERNAL CONSULTANTS DRAWINGS AND REFERENCE SHOULD BE MADE TO THE INDIVIDUAL CONSULTANT DRAWINGS FOR EXACT DIMENSIONS & CO-ORDINATION PRIOR TO ONSITE INSTALLATION.
DISCREPANCIES AND/OR AMBIGUITIES WITHIN THIS DRAWING AND INFORMATION PROVIDED ELSEWHERE, MUST BE REPORTED IMMEDIATELY TO ALTERNATIVE HEAT LTD. FOR CLARIFICATION BEFORE PROCEEDING WITH INSTALLATION.
ALL WORKS ARE TO BE CARRIED OUT IN ACCORDANCE WITH THE LATEST BRITISH STANDARDS AND CODES OF PRACTICE UNLESS SPECIFICALLY DIRECTED OTHERWISE IN THE SPECIFICATION.

CT	FIRST ISSUE	OF	EE	28.05.20
Rev	Revision Description	Draw	Chk	Date

status:
CONSTRUCTION

client:
HSC Belfast Health and Social Care Trust

project title:
OXYGEN GENERATION UNITS

drawing title:
STRUCTURAL SLAB DETAILS

drawing no:
WJM2001-ALT-ZZ-XX-DR-S-1002

date:
28/05/2020 12:37:32

drawn by: OF

checked by: EE

alternativeHEAT
Commercial Energy Solutions
Head Office: Unit 18 - 19 Scarva Road Industrial Estate, Scarva Road, Banbridge, Co. Down, BT32 3QD
Tel: +44 (0) 28 437 70700 Fax: +44 (0) 28 437 78404
info@alternativeheat.co.uk | www.alternativeheat.co.uk