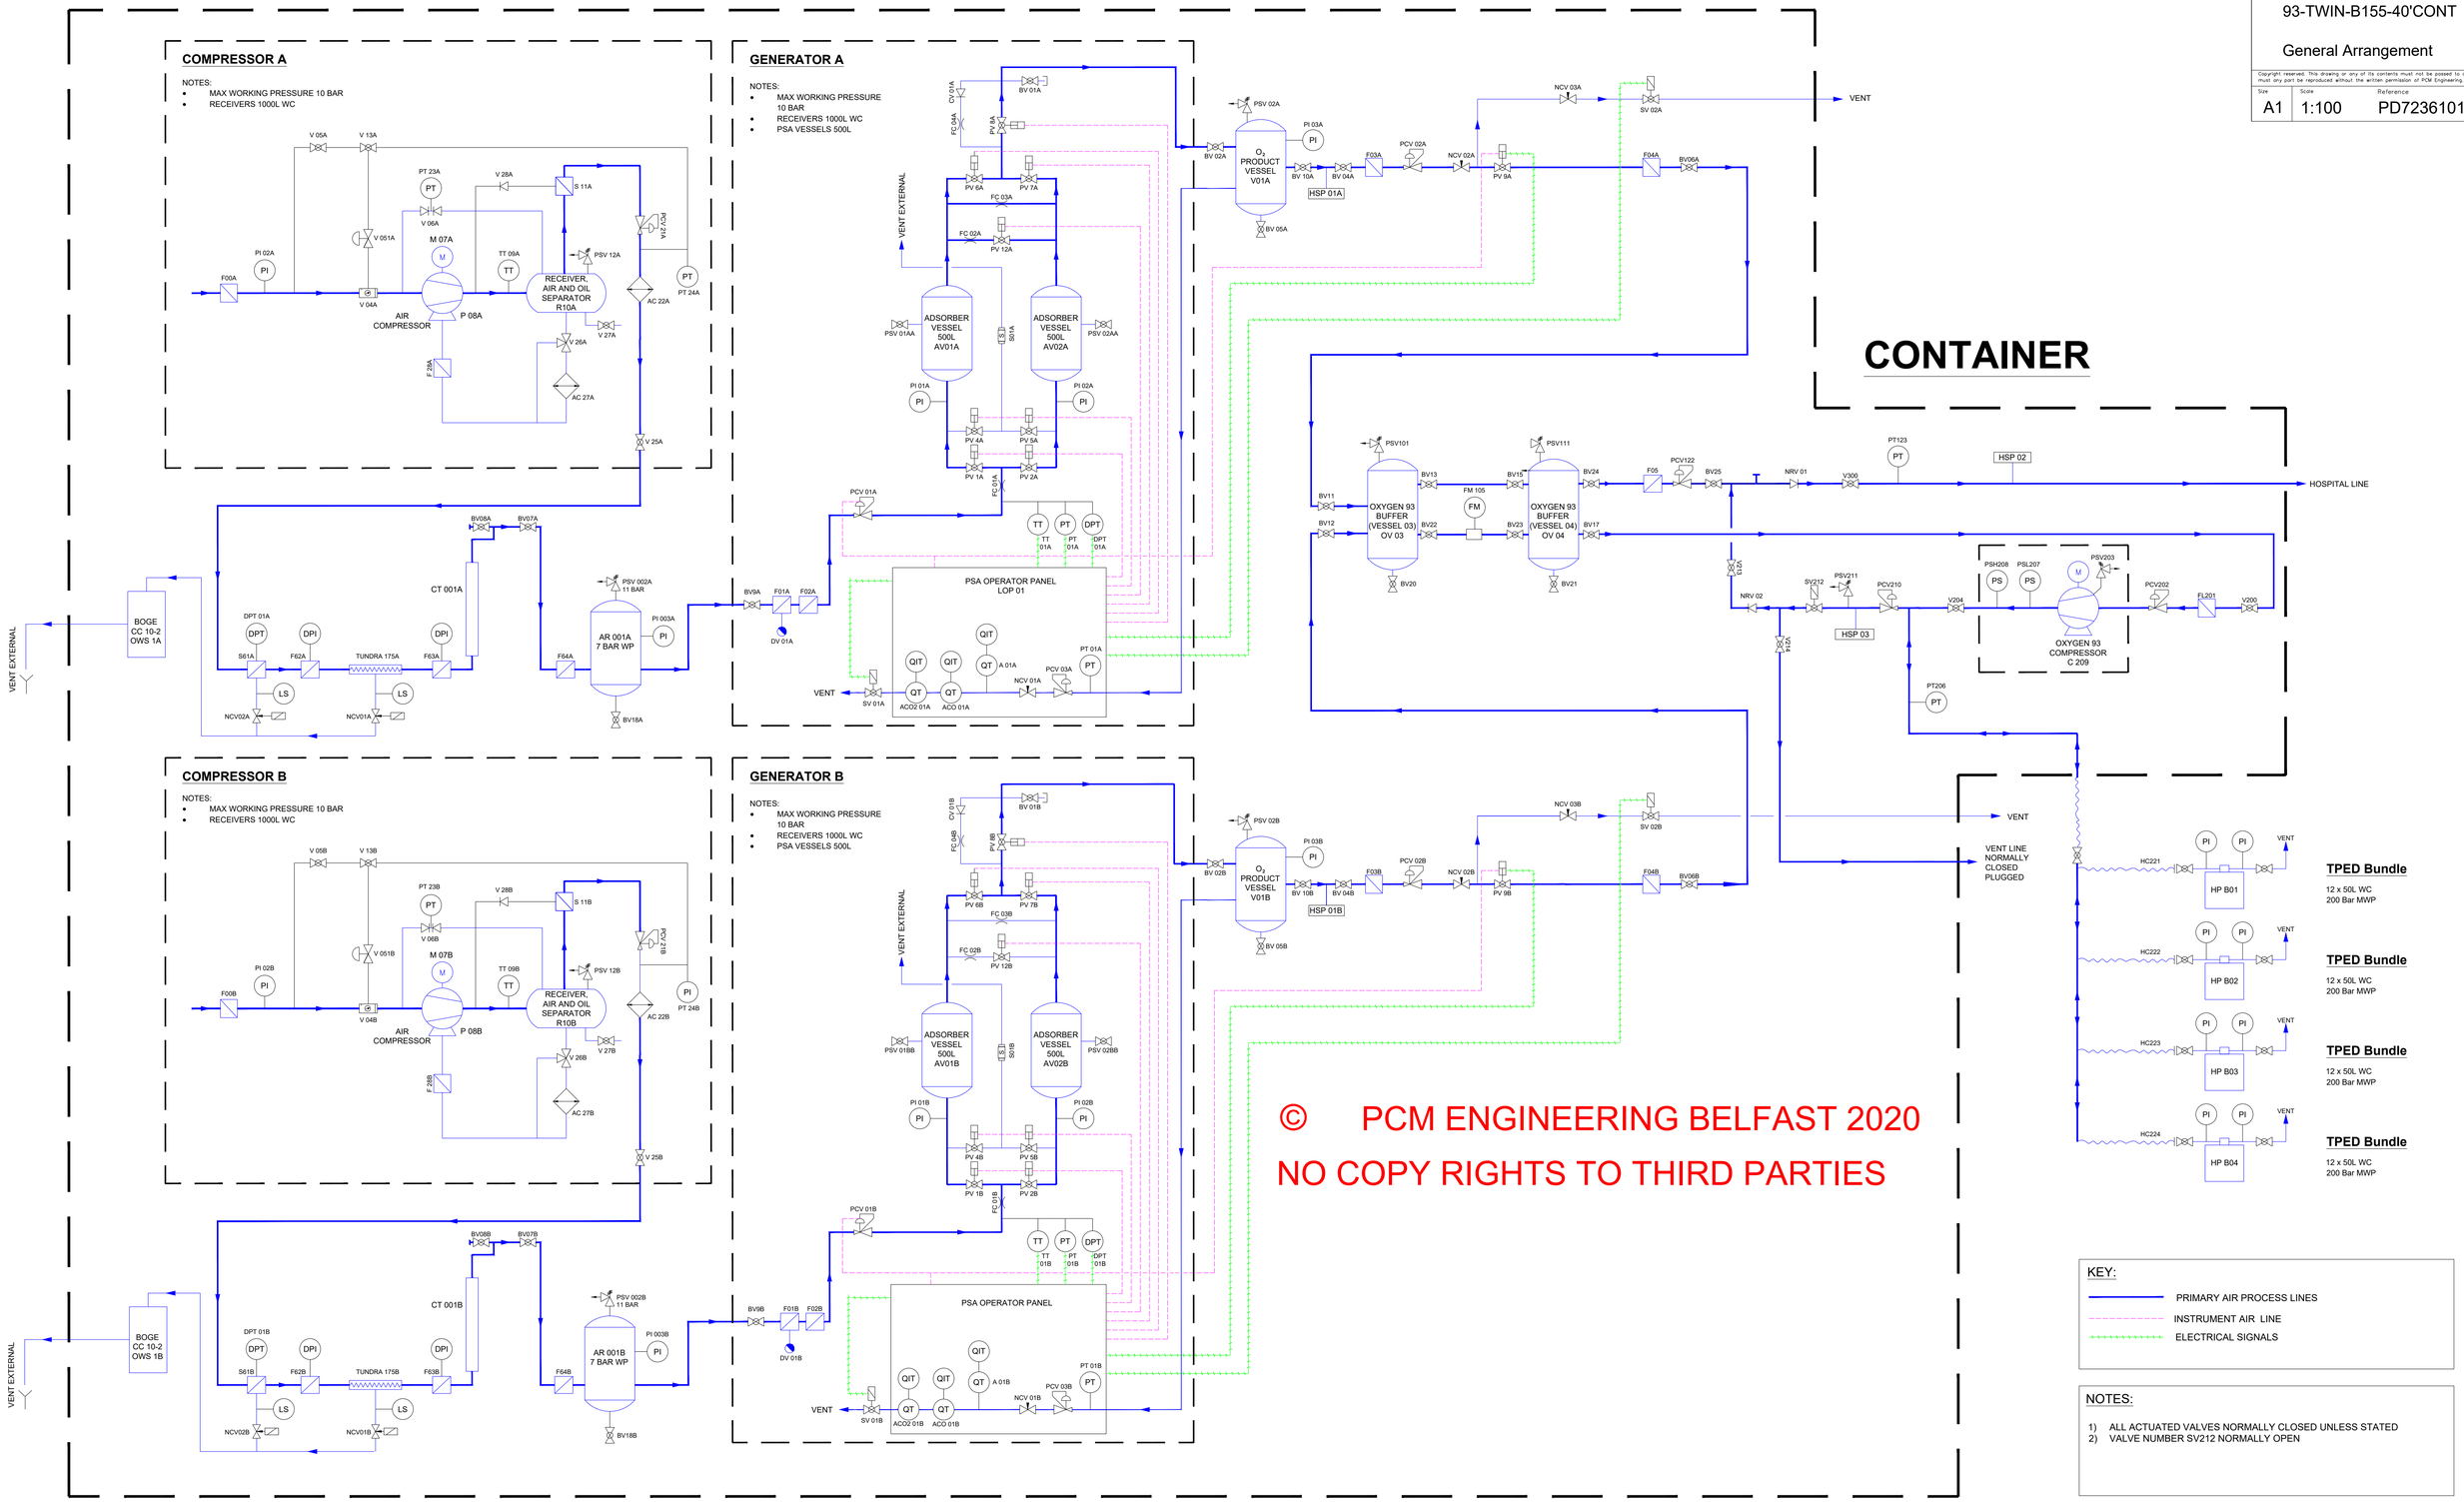


© PCM ENGINEERING BELFAST 2020
NO COPY RIGHTS TO THIRD PARTIES

Title: PCM-OXYGEN. 93-TWIN-B155-40'CONT — General Arrangement

Copyright reserved. This drawing or any of its contents must not be passed to a third party, neither must any part be reproduced without the written permission of PCM Engineering.

Size	Scale	Reference	Iss.
A1	1:100	PD7236101	E

REVISIONS

Iss.	Description	Name	Date
A	Issued For Information	B.McA.	22/04/20
B	Revised as per comments	JMC	13/05/20
C	Revised as per comments	JMC	14/05/20
D	Revised as per comments	JMC	15/05/20
E	As Built	JMC	02/06/20
F	As Built - Final	JMC	17/06/20

NOTES

pcm engineering
Tel: +44 (0)28 9077 7370 Fax: +44 (0)28 9077 7023
Unit 3, Duncrue Crescent, Belfast, BT3 9BW
www.pcmengbelfast.co.uk

Project: Medical — O2 Generation

Title: PCM-OXYGEN. 93-TWIN-B155-40'CONT — General Arrangement

Designed	Date	Checked	Date
B.McA.	10/04/20		
Drawn	Date	Approved	Date
J.McC	11/05/20		

Copyright reserved. This drawing or any of its contents must not be passed to a third party, neither must any part be reproduced without the written permission of PCM Engineering.

Size	Scale	Reference	Iss.
A1	1:100	PD7236101	FW